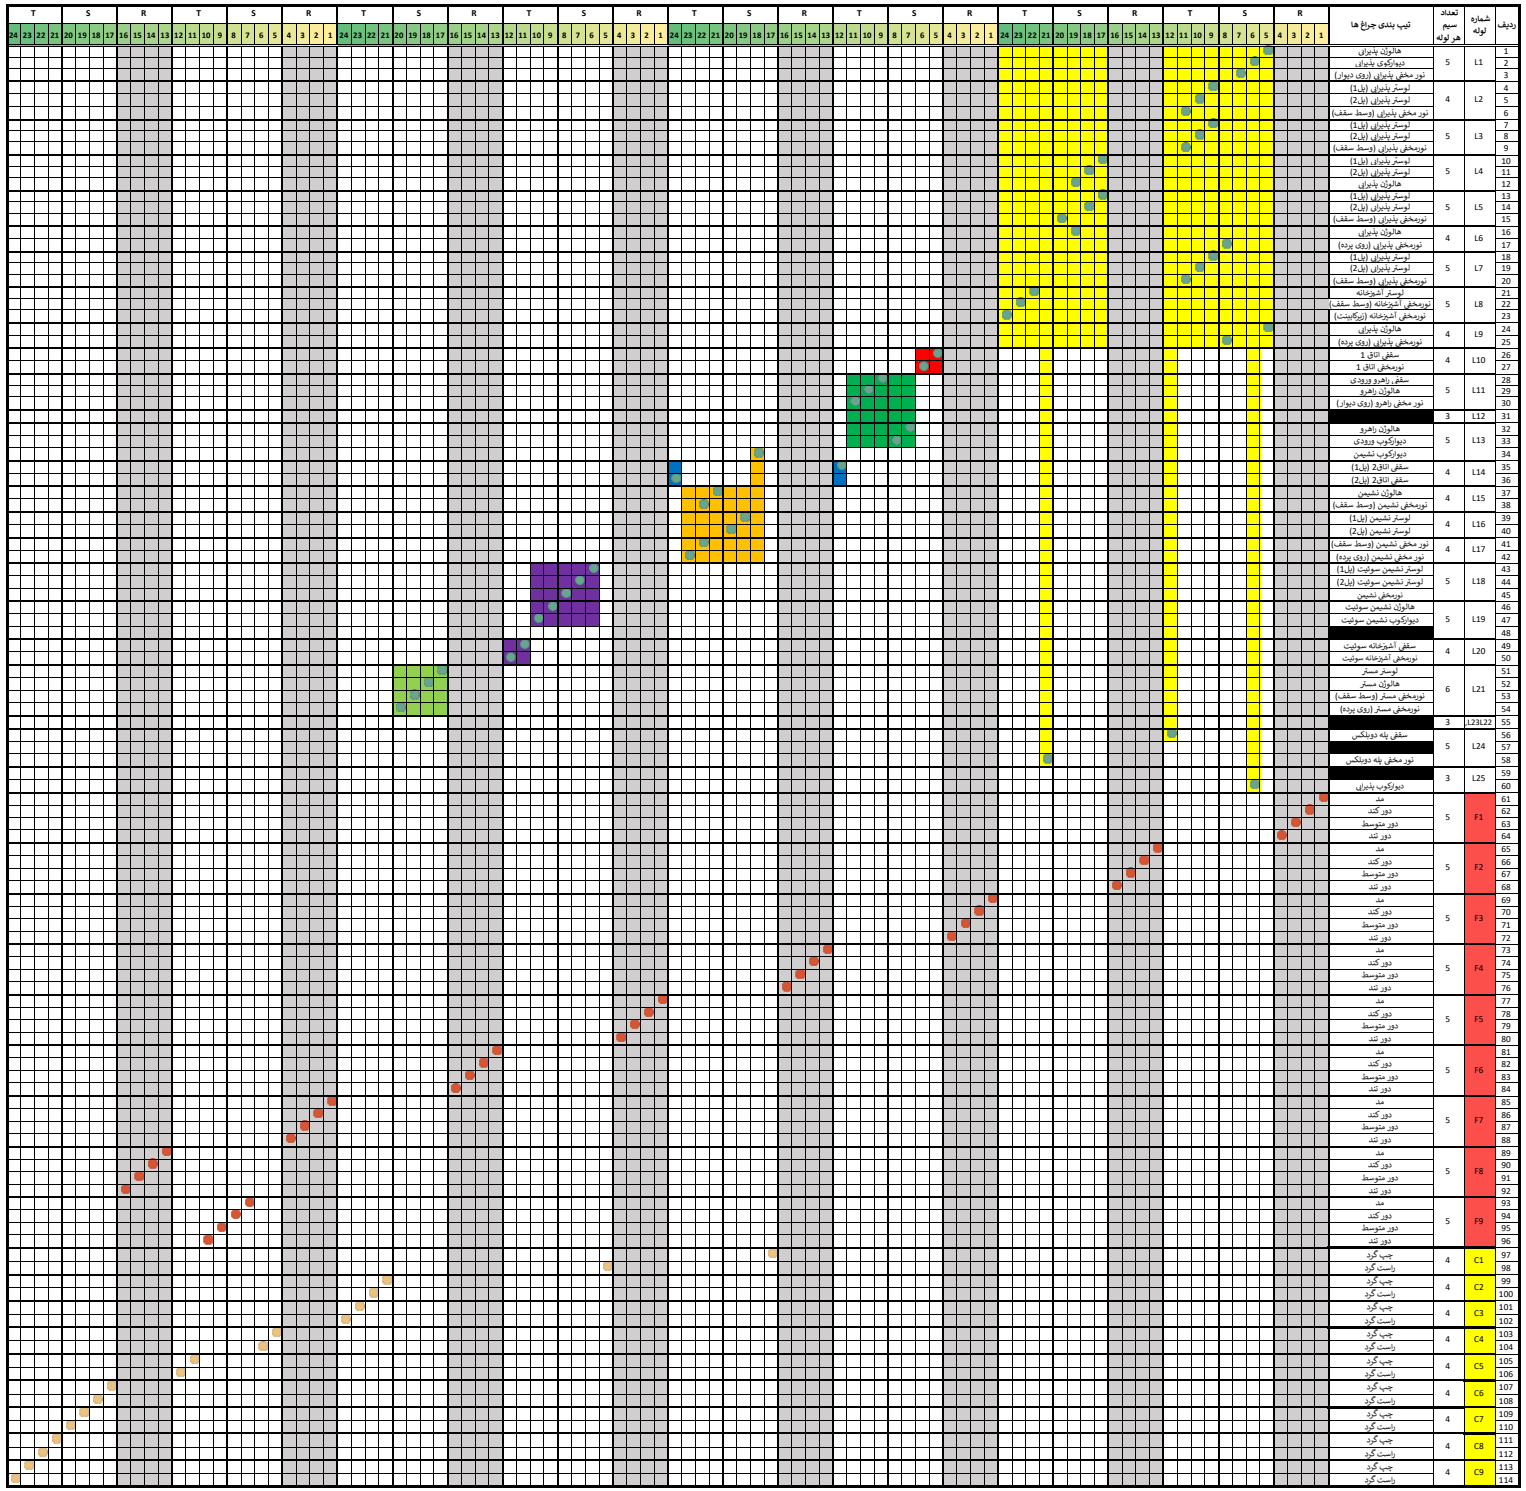


ردیف	شماره لوله	تعداد سیم هر لوله	تیپ بندی چراغ ها
1	L1	5	هالوژن پذیرائی
2			دیوارکوب پذیرائی
3			نور مخفی پذیرائی (روی دیوار)
4	L2	4	لوستر پذیرائی (بل1)
5			لوستر پذیرائی (بل2)
6			نور مخفی پذیرائی (وسط سقف)
7	L3	5	لوستر پذیرائی (بل1)
8			لوستر پذیرائی (بل2)
9			نورمخفی پذیرائی (وسط سقف)
10	L4	5	لوستر پذیرائی (بل1)
11			لوستر پذیرائی (بل2)
12			هالوژن پذیرائی
13	L5	5	لوستر پذیرائی (بل1)
14			لوستر پذیرائی (بل2)
15			نورمخفی پذیرائی (وسط سقف)
16	L6	4	هالوژن پذیرائی
17			نورمخفی پذیرائی (روی پرده)
18	L7	5	لوستر پذیرائی (بل1)
19			لوستر پذیرائی (بل2)
20			نورمخفی پذیرائی (وسط سقف)
21	L8	5	لوستر آشپزخانه
22			نورمخفی آشپزخانه (وسط سقف)
23			نورمخفی آشپزخانه (زیرکابینت)
24	L9	4	هالوژن پذیرائی
25			نورمخفی پذیرائی (روی پرده)
26	L10	4	سقفی اتاق 1
27			نورمخفی اتاق 1
28	L11	5	سقفی راهرو ورودی
29			هالوژن راهرو
30			نور مخفی راهرو (روی دیوار)
31	L12	3	
32	L13	5	هالوژن راهرو
33			دیوارکوب ورودی
34			دیوارکوب نشیمن
35	L14	4	سقفی اتاق2 (بل1)
36			سقفی اتاق2 (بل2)
37	L15	4	هالوژن نشیمن
38			نورمخفی نشیمن (وسط سقف)
39	L16	4	لوستر نشیمن (بل1)
40			لوستر نشیمن (بل2)
41	L17	4	نور مخفی نشیمن (وسط سقف)
42			نور مخفی نشیمن (روی پرده)
43	L18	5	لوستر نشیمن سولیت (بل1)
44			لوستر نشیمن سولیت (بل2)
45			نورمخفی نشیمن
46	L19	5	هالوژن نشیمن سولیت
47			دیوارکوب نشیمن سولیت
48			
49	L20	4	سقفی آشپزخانه سولیت
50			نورمخفی آشپزخانه سولیت
51	L21	6	لوستر مستر
52			هالوژن مستر
53			نورمخفی مستر (وسط سقف)
54			نورمخفی مستر (روی پرده)
55	L23L22	3	
56	L24	5	سقفی پله دوبلکس
57			
58			نور مخفی پله دوبلکس
59	L25	3	
60			دیوارکوب پذیرائی
61	F1	5	مد
62			دور کند
63			دور متوسط
64			دور تند
65	F2	5	مد
66			دور کند
67			دور متوسط
68			دور تند
69	F3	5	مد
70			دور کند
71			دور متوسط
72			دور تند
73	F4	5	مد
74			دور کند
75			دور متوسط
76			دور تند
77	F5	5	مد
78			دور کند
79			دور متوسط
80			دور تند
81	F6	5	مد
82			دور کند
83			دور متوسط
84			دور تند
85	F7	5	مد
86			دور کند
87			دور متوسط
88			دور تند
89	F8	5	مد
90			دور کند
91			دور متوسط
92			دور تند
93	F9	5	مد
94			دور کند
95			دور متوسط
96			دور تند
97	C1	4	چپ گرد
98			راست گرد
99	C2	4	چپ گرد
100			راست گرد
101	C3	4	چپ گرد
102			راست گرد
103	C4	4	چپ گرد
104			راست گرد
105	C5	4	چپ گرد
106			راست گرد
107	C6	4	چپ گرد
108			راست گرد
109	C7	4	چپ گرد
110			راست گرد
111	C8	4	چپ گرد
112			راست گرد
113	C9	4	چپ گرد
114			راست گرد